

Монтажный план потолочного оборудования, 1:25

Привязки — от черновых стен (без штукатурки и плитки), мм. Трассы ThermoDuct — серым, для ориентира.

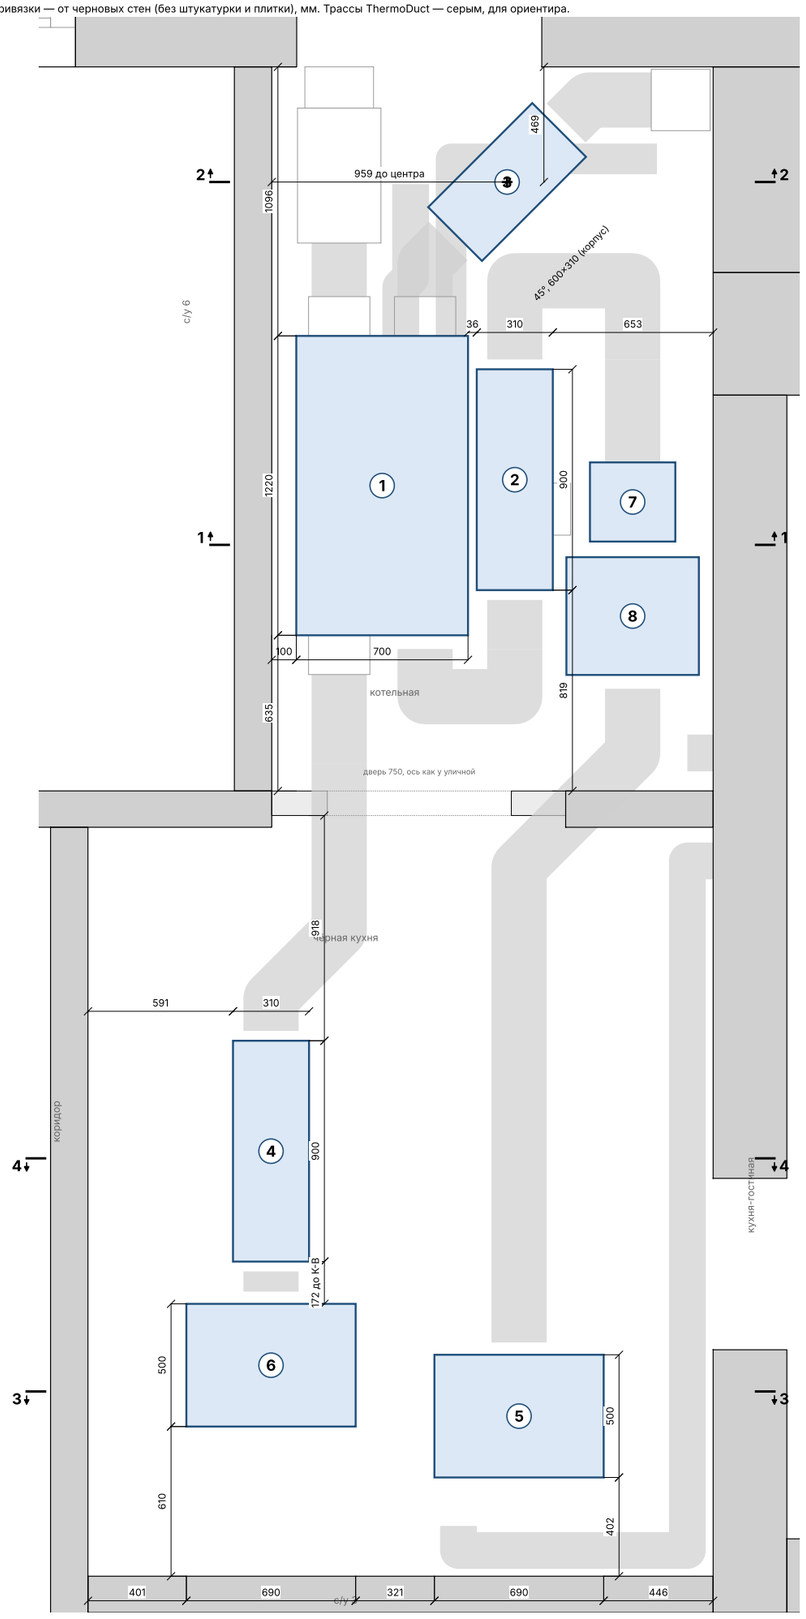


Разрез 1-1

по ПВУ, глушителю притока и догревателю ECONOW, вид на север (к улице)

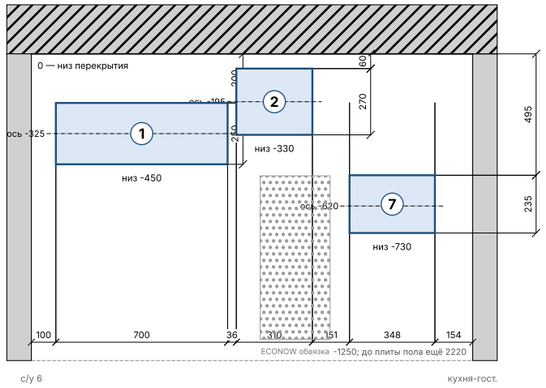


Разрез 2-2

по центру глушителя выброса (он под 45°: в сечении 438), вид на север

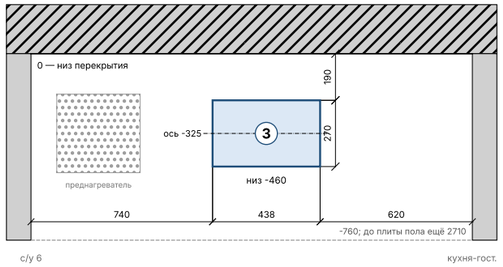


Разрез 3-3

по коллекторам К-В и К-П, вид на юг (на с/у 3)

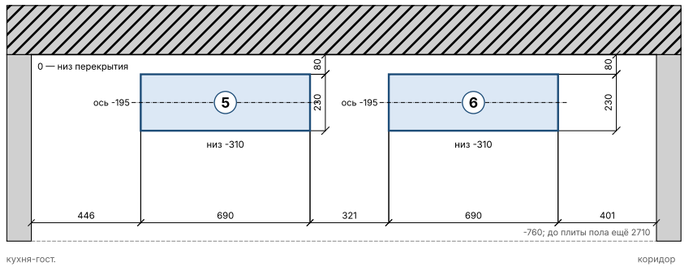

Разрез 4-4

по глушителю вытяжки, вид на юг

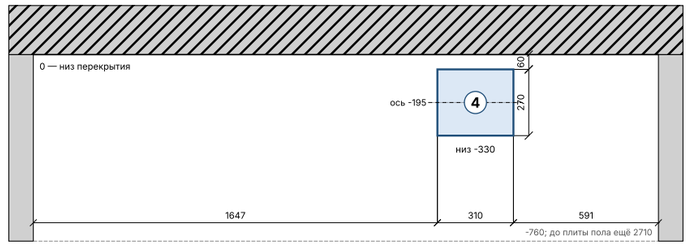

Потолочное оборудование: размеры и отметки от потолка, мм

№	элемент	габарит (Д×Ш×В)	верх	ось	низ	примечание
1	ПВУ Allston-VH5.5	1220×700×250	-200	-325	-450	люки и фильтры снизу — зона 700×1080 под ПВУ свободна
2	Глушитель притока D200-900	980×310×270	-60	-195	-330	с патрубками 2×40; вдоль ПВУ на север
3	Глушитель выброса D200-600	680×310×270	-190	-325	-460	под 45°, на патрубке ПВУ через отвод 45°
4	Глушитель вытяжки D200-900	980×310×270	-60	-195	-330	в чёрной кухне, на оси К-В
5	Коллектор приточный К-П	690×500×230	-80	-195	-310	вход сзади (с севера) по центру; 6 верхних спереди + 5 сбоку
6	Коллектор вытяжной К-В	690×500×230	-80	-195	-310	вход сзади по центру; 11 спереди + 3 сбоку
7	ECONOW догреватель WHR	323×348×235	-495	-620	-730	одно изделие с модулем (923 вдоль потока); обвязка на запад, низ −1163
8	ECONOW модуль ПК-4.ВД	480×540×313	-482	-620	-795	над крышкой 300 свободно для выемки кассеты

- Отметки — от низа существующего перекрытия (потолок = 0), вниз со знаком «−». Высота помещения 3470 до плиты пола.
- Привязки на плане — от черновых стен; после штукатурки и плитки (~30 на стену) размеры до чистовой стены меньше на 30.
- ПВУ, глушители и коллекторы подвешиваются к перекрытию на шпильках с виброизолирующими подвесами; ПВУ — по паспорту (4 точки, кронштейны на корпусе).
- Преднагреватель, заслонки, переходы 200/150 и обвязка догревателя (пунктир) висят на трассе, их отметки — по листу Tula_kotelnaya_v8.pdf.