

План котельной и чёрной кухни (пом. 5), 1:25


Все отметки — от низа существующего перекрытия (потолок = 0), мм, вниз со знаком «−». Высота помещения 3470 (до плиты пола).

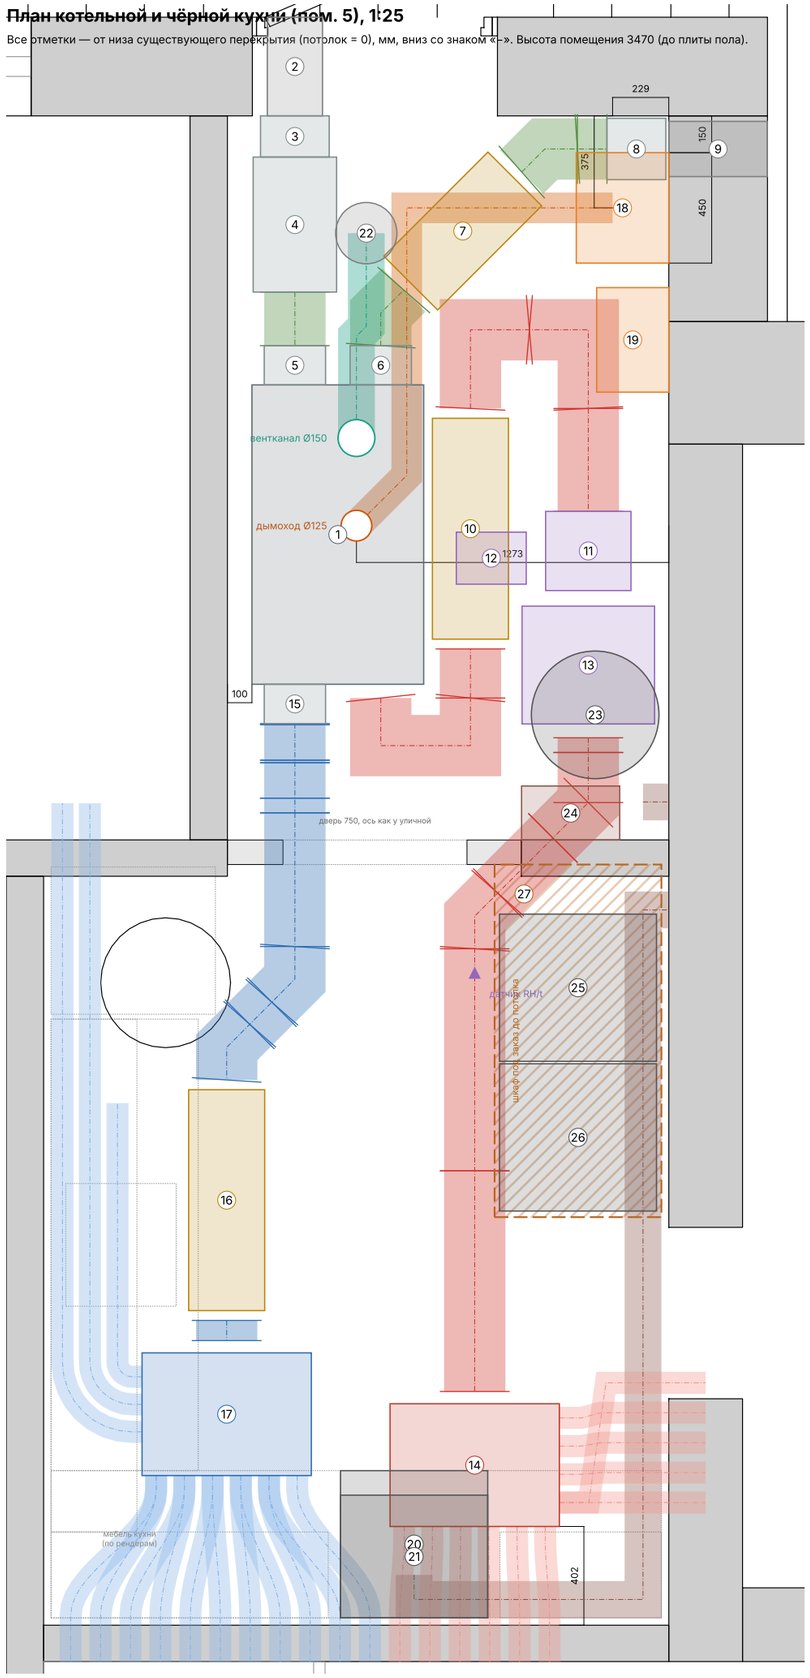

Развёртка А: вид на восток (север слева), 1:30

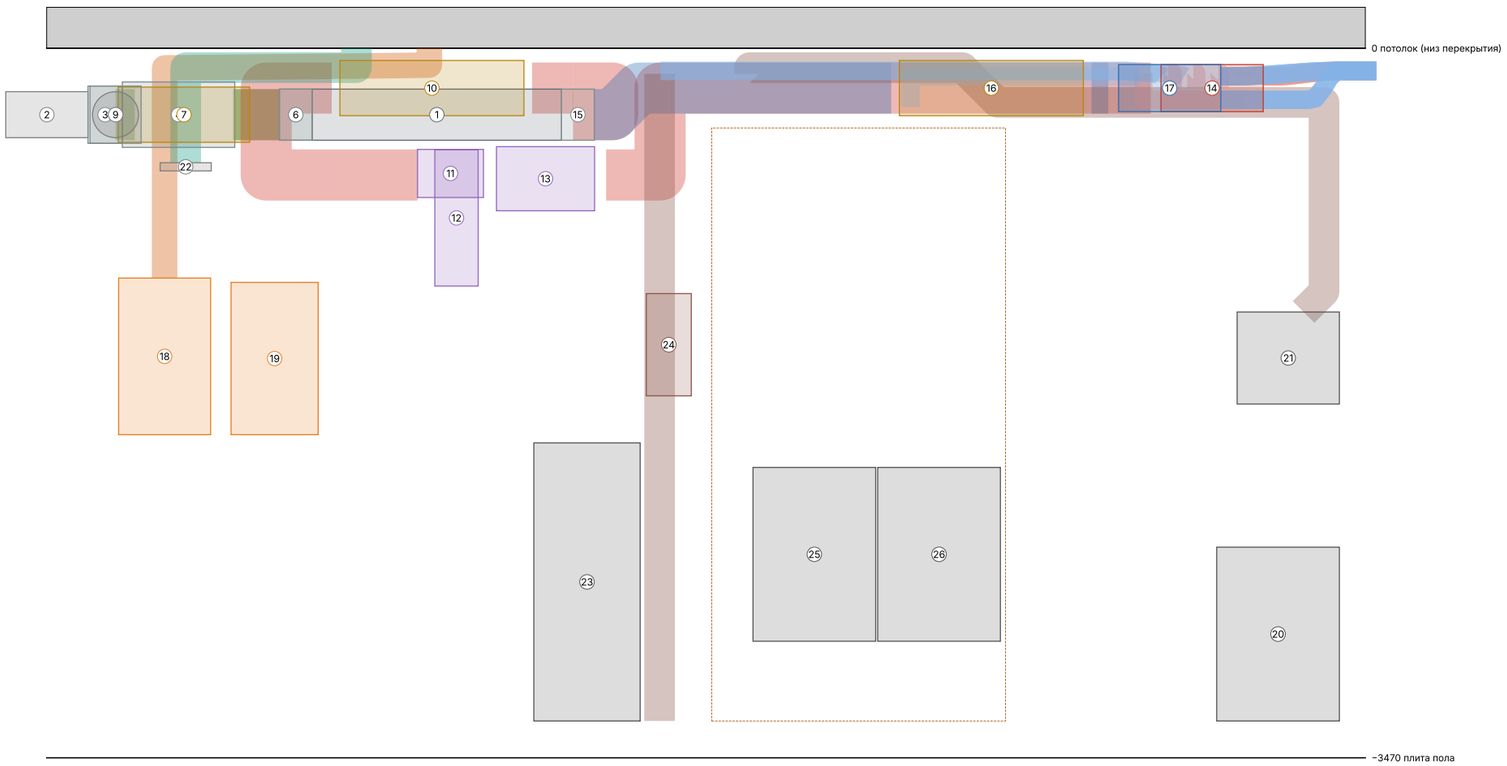

Развёртка Б: вид на север, 1:30

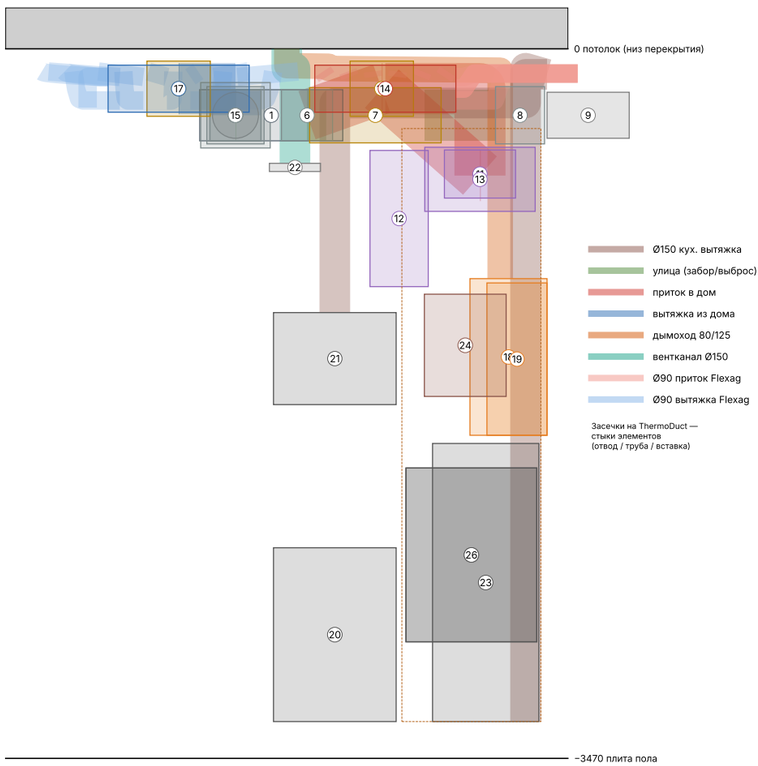

Оборудование и отметки от потолка, мм

№	наименование	низ	верх	ось	примечание
1	ПВУ	-450	-200	-325	SKOYOD Allston-VH5.5, 1220×700×250
2	решётка забора	-438	-213	-325	ThermoDuct Ø225 в стене до фасада, решётка сна
3	заслонка	-465	-185	-325	с электроприводом
4	преднагреватель	-485	-165	-325	водяной
5	переход 200/150 забор	-450	-200	-325	ThermoDuct 160/200 L104 + патрубок ПВУ
6	переход 200/150 выброс	-450	-200	-325	ThermoDuct 160/200 L104 + патрубок ПВУ
7	глушитель выброса	-460	-190	-325	Турков прямоуг. D200-600, под 45° к выходу
8	заслонка выброса	-465	-185	-325	с электроприводом, НЗ
9	решётка выброса	-438	-213	-325	ThermoDuct Ø225 в сущ. отверстии Ø250, решётка
10	глушитель притока	-330	-60	-195	Турков прямоуг. D200-900
11	ECONOW догреватель	-730	-495	-620	водяной WHR 300×150, единое изделие с модулем
12	ECONOW обвязка	-1163	-497		обвязка догревателя: насос, 3-ход. кран, фильт
13	ECONOW модуль	-795	-482	-620	ПК-4.ВД по STEP: корпус 480×540×313, в котельн
14	К-П	-310	-80	-195	Flexag CMP-FLD 200/90×12, верх −80; спереди то
15	переход 200/150 вытяжка	-450	-200	-325	ThermoDuct 160/200 L104 + патрубок ПВУ
16	глушитель вытяжки	-330	-60	-195	Турков прямоуг. D200-900
17	К-В	-310	-80	-195	Flexag CMP-FLD 200/90×12 (12 спереди 2×6 + по
18	котёл	-1890	-1124		Baxi LUNA Duo-tec MP 1.35, 450×377×766
19	электрокотёл AMPERA Pro	-1890	-1145		BAXI AMPERA Pro 9–24 кВт, 426×294×745, справа
20	газовая плита	-3290	-2440		газовая варочная панель в столешнице у южной с
21	зонт вытяжки	-1740	-1290		каминная вытяжка 600 (по рендеру), низ на 700
22	диффузор вентканала	-600	-560	-580	потолочный диффузор Ø150 (корпус Ø250), низ −6
23	бойлер AMET 200	-3290	-1930		Termica AMET 200 INOX, напольный Ø520 H1360, п
24	шкаф ECONOW	-1700	-1200		500×400×220 на перегородке над бойлером, между
25	стиральная	-2900	-2050		на подиуме 390, у узкой колонки, 600×640×850
26	сушильная	-2900	-2050		на подиуме 390, рядом со стиральной
27	шкаф: стиральная/сушильная	-3290	-390		под заказ до потолка ГКЛ (2900 от чистого пола

- v8 (05.11, по 3D v8): ПВУ на оси −325 (ось сущ. отверстия выброса). Глушители Турков D200-900. Под заказ ThermoDuct: калач 1 (с переходом 150/200), 2 отвода 90° R204 после модуля и 2 отвода 45° R204 на вытяжке; остальное — штатные отводы.
- Приток: ПВУ → калач 1 R194 под заказ с переходом 150/200, наклонный (366 вбок, 130 вверх) → вставка 200 → глушитель 900 на север под потолком (ось -195, верх −60, x 14590) → калач 2 из двух штатных отводов 90° + вставка 190 в раструбах, в наклонной плоскости (480 к стене кухни-гостиной, 425 вниз) → ECONOW на юг.
- ECONOW: догреватель + модуль ПК-4.ВД — одно изделие 923 вдоль потока, в котельной у стены кухни-гостиной, ось x 15070, -620; у 11964…12886. Верх крышки модуля −482, над ней 300 на выемку кассеты свободно. Обвязка догревателя на запад, низ −1163 (≈2.13 м от чистого пола).
- После модуля: отвод 90° R204 вверх в 20 от перегородки (подъём 425 в котельной) → отвод 90° R204 сразу на юго-запад под потолком (ось -195) сквозь перегородку → отвод 45° на юг → К-П (верх −80). К-П: x 14262…14952, y 8750…9250; К-В: x 13251…13941. Путь от модуля до датчика RH 1.39 м (паспорт ≥1 м); датчик на воздуховоде в чёрной кухне, рядом люк в ГКЛ.
- Вытяжка: К-В (верх −80) → глушитель 900 под потолком (ось -195) → смещение 278 на восток штатными 45° → сквозь перегородку под потолком → в котельной опуск 130 двумя отводами 45° R204 под заказ на ось ПВУ → ПВУ. Запас 82 мм.
- Ø150 кухонной вытяжки: от зонта вверх, дальше на одном уровне (ось -265, без провисов) в шкафах вдоль стен, над дверью — в коробе ГКЛ, в существующее отверстие в стене кухни-гостиной под трубами Ø90.
- Трубы Ø90 Flexag: П7–П11 от К-П сразу вверх под потолок и в 5 отверстий стены кухни-гостиной (y 8847…9335, шаг 122) над Ø150. Остальные — в отверстия стены с/у 3 (17 шт., шаг 122, ось -111) без перехлёстов. К-В отодвинут от стены с/у на 610.
- Дымоход коакс. 80/125: вверх от котла до потолка, по потолку на запад до x 14330, на юг над ПВУ, отводом 45° в южную проходку Ø125; уклон к котлу 1 см/м.
- Потолок ГКЛ чёрной кухни 12.5 по профилю: низ −390 от перекрытия = 2900 от чистого пола (чистый пол = плита +180), закрывает все воздуховоды.
- Дверь котельная — чёрная кухня на одной оси с дверью на улицу (x 13825…14575), перегородка однородная.
- Бойлер Termica AMET 200 INOX (Ø520, H1360) у стены кухни-гостиной: x 14838…15358, y 11797…12317. Шкаф управления ECONOW 500×400×220 на перегородке над бойлером (x 14798…15198). Шкаф под стиральную и сушильную машины (по рендеру): до потолка ГКЛ, узкая колонка 160 у перегородки, подиум 390 с двумя ящиками, машины рядом (стиральная у колонки), над ними открытые полки.
- Проверка 3D: пересечений нет; мин. зазоры 20 (бойлер / шкаф — стояк острова; соседние Ø90).