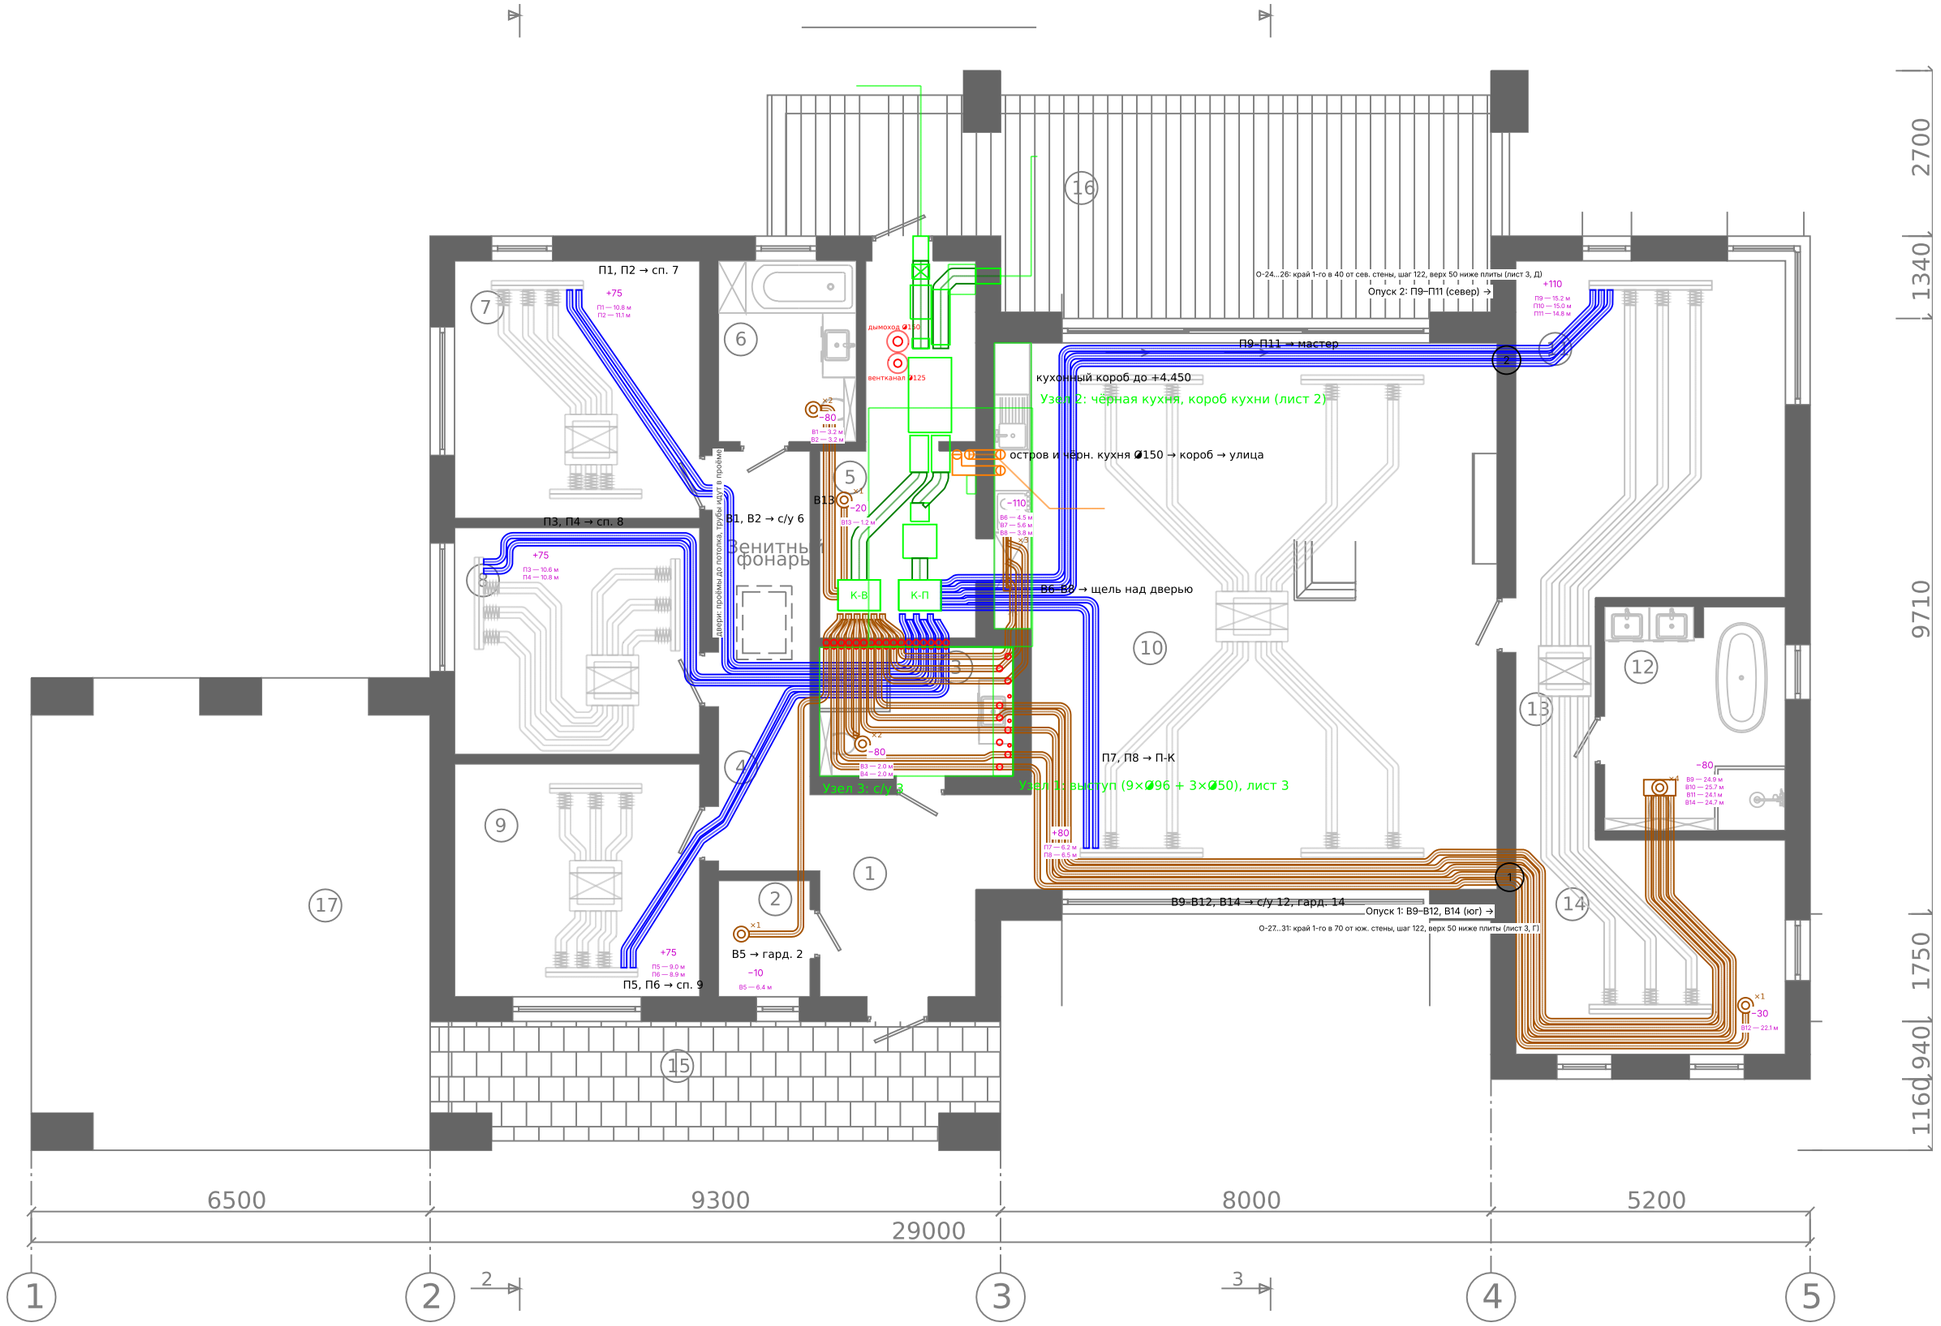


Обозначения

- Приток Ø90 (П), Flexag FL90
- Вытяжка Ø90 (В)
- Потолочный пленум Flexag, ×N — число Ø90
- Коллектор: К-П приток, К-В вытяжка
- Проходка Ø90 в полосе стены
- Узлы 1–3; узел у кухни — лист 2
- Ø160 кондиционеров (фон)

Трассы Ø90: расход м³/ч — длина, м

П1 Спальня 7 38 — 10.8	В9 С/у 12 20 — 24.9
П2 Спальня 7 38 — 11.1	В14 С/у 12 20 — 24.7
П3 Спальня 8 38 — 10.6	В11 С/у 12 20 — 24.1
П4 Спальня 8 38 — 10.8	В6 Кухня 37 — 4.5
П5 Спальня 9 38 — 9.0	В7 Кухня 37 — 5.6
П6 Спальня 9 38 — 8.9	В8 Кухня 37 — 3.8
П7 Кухня-гостин. 40 — 6.2	В3 С/у 3 40 — 2.0
П8 Кухня-гостин. 40 — 6.5	В4 С/у 3 40 — 2.0
П9 Мастер-спальн 37 — 15.2	В5 Гардероб. 2 10 — 6.4
П10 Мастер-спальн 37 — 15.0	В1 С/у 6 40 — 3.2
П11 Мастер-спальн 37 — 14.8	В2 С/у 6 40 — 3.2
В12 Гардероб. 14 30 — 22.1	В13 Постирочная 20 — 1.2
В10 С/у 12 20 — 25.7	

Итого ≈ 272 м, в т.ч. в котельной 16 м. Приток 11 линий, вытяжка 14.

Схема

П7–П11 — с бока К-П одним рядом в стену, над дверью (О-1…О-5), в коробе вверх за потолок гостиной.
Остальные 17 — в с/у 3 через перегородку одним рядом (Р-1…Р-17; В1, В2, В13 остаются в чёрной кухне). П1, П2 — западнее фонаря.
В6–В12, В14 — вверх через выступ плиты (лист 3).
Ø90 ≤ 2,5 м/с. Из чёрной кухни в стену — без пересечений, перехлёст — в с/у 3 за потолком ровной сеткой (и в с/у 6).
Повороты Ø90 — дугой, R ≈ 150 по оси.
У диффузоров: расход, м³/ч (+ приток, − вытяжка), под ним — длины трасс.

Сноски

1. Опуск 1 (юг) и опуск 2 (север): переход гостиная → мастер-зона в углах, трубы спускаются под потолок мастер-зоны (+3,200) и зашиваются декоративным коробом (согласовать с дизайнером).
2. Диффузоры с/у — по оси унитаза, 700 мм от стены с унитазом.
3. Кухня: одна щель 1×30, L=900 над дверью в чёрную кухню (лист 2), 3 врезки Ø90 в камеру. Трубы — в коробе над выступом и пеналом.
4. Пом. 2: диффузор в центре левой половины по оси двери.
5. Врезки Ø90 в КСД — с комнатной стороны (мастер, 7, 8, 9, гостиная).
6. Два Ø150 (остров и зонт чёрной кухни) — рядом вверх в котельной → стена → короб → 3-й ряд верхней стены → решётки (лист 2).
7. Канал в полу острова — Ø150 (?), прорабатывается отдельно.
8. Гардероб 14: В9–В12, В14 обходят щель В-1 с юга, без пересечений с Ø160. С/у 12: 4 трубы через стену по оси унитаза (2 слева, 2 справа).
9. Котельная: дымоход Ø150 и вентканал Ø125 — по АС (план кровли), ПВУ сдвинута к стене кухни и их не закрывает (лист ОВК v10).
10. Отверстия Ø90 в газоблоке просверлены: Ø102, перемычка 20 (шаг 122); верх на 60 ниже плиты в чёрной кухне, на 50 — в гостиной; опуски 1, 2 — по факту: 70 от юж. и 40 от сев. стены до края 1-го (лист 3, Г, Д).

Частный жилой дом, г. Тула. Вентиляция и кондиционирование
План этажа. Вентиляция: разводка Flexag Ø90 от коллекторов (на согласование)
Стадия: эскиз. Разводка Ø90, версия 14 от 02.11.2026. Лист 1. Масштаб 1:100 (А3)
Ø160 кондиционеров — серым фоном (лист ОВК v10). Фреон, дренажи, мебель на этом листе не показаны