
План этажа

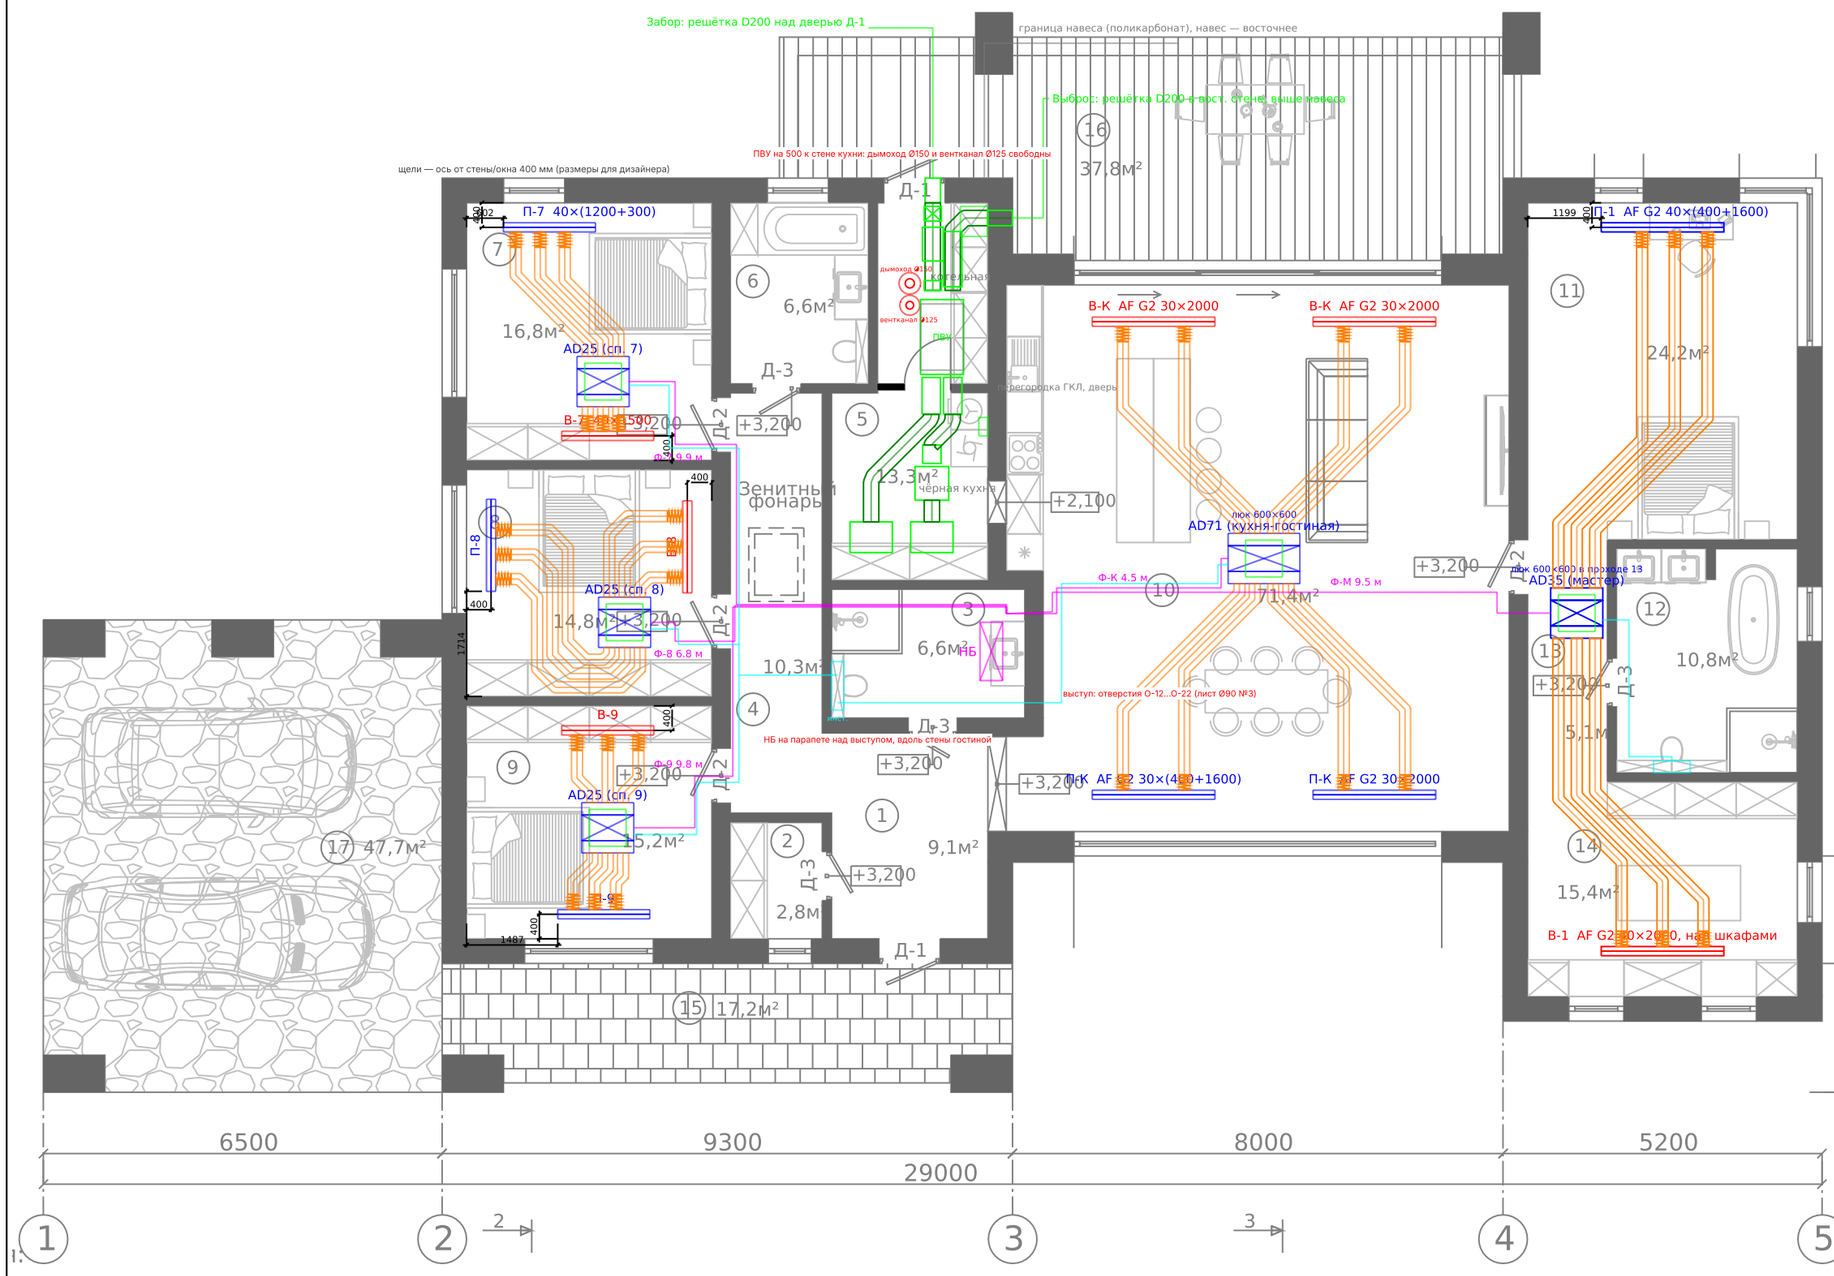

Трассы фреона, Haier 5U125

в плане + 2 м (подъём, фасад, НБ на парапете)
Ф-7 (AD25): 9.9 + 2 = 11.9 м
Ф-8 (AD25): 6.8 + 2 = 8.8 м
Ф-9 (AD25): 9.8 + 2 = 11.8 м
Ф-М (AD35): 9.5 + 2 = 11.5 м
Ф-К (AD71): 4.5 + 2 = 6.5 м
Сумма: 50.5 м
SL (40 м на блок / 120 м сумма) — с запасом.
SN (25 м / 100 м) — проходит с запасом.
Все 5 трасс сводятся к зоне подъёма над выступом с/у 3:
3 трассы спален (7, 8, 9) — через 3×Ø50 в выступе;
Ф-М, Ф-К — по потолку гостиной к выступу, через О-14 (Ø96)
к НБ над выступом (лист Ø90 №3).

Обозначения

- Щелевой подачи (П), Flow AF G2 + КСД
- Щелевой возврата (В), Flow AF G2 + КСД
- Блок AD в габаритах + камеры 200 мм
- Сервисный люк 600×600
- Ø160 оцинк. + ППЭ 10 мм (нар. 180 мм)
- Гибкая вставка Ø160 L=250 у КСД
- Фреонопровод (пара + кабель)
- Дренаж AD → воронка в инсталляции с/у
- Размеры щелей для дизайнера, мм
- Оборудование вентиляции (котельная)
- ISO-воздуховод DN200 (нар. ≈250 мм)
- Перегородка ГКЛ с дверью: котельная / чёрная кухня
- Дымоход Ø150 и вентканал Ø125 в плите (АС)
- Граница навеса террасы (поликарбонат)

Щели: размеры (ось щели, мм)

Спальни 7, 8, 9 и мастер: ось щели в 400 мм от стены
с окном (подача и возврат). Остальные размеры — на плане.
Гостиная (предв.): П-К (400+1600) и 2000 у юж. окна,
В-К 2000 у сев. окна. Мастер: П-1 у сев. окна.

Дренажи (помпы встроены, уклон ≥ 1 %)

Сп. 7, 8, 9 и AD71 — в инсталляцию с/у 3: короб до потолка,
ревизионный люк, воронки с сифонами (4 шт.).
AD35 (мастер) — в инсталляцию с/у 12 (сифон, люк).

Проверить на замерах

1. Высота выступа над с/у 3, место НБ на парапете.
2. Толщина плиты в зоне подъёма (монолит ≈200).
3. Мастер: AD35 над проходом 13, люк в проходе.
4. Коридор 4: зазор фонарь–стена 300 мм.
5. Инсталляции с/у 3 и 12: место воронок и люков.

Частный жилой дом, г. Тула. Вентиляция и кондиционирование
План этажа. Кондиционирование в масштабе, дренажи, фреон; оборудование вентиляции в пом. 5
Стадия: эскиз для замеров. Версия 10 / Ø90 версия 12 от 02.11.2026. Масштаб 1:100 (лист А3)
Котельная: дымоход Ø150 и вентканал Ø125 — по АС (план кровли), проверить по месту. Ø90 — Tula_V90_v12